BUILD PLAN SKETCH, PLAN NOT YET BUILT

DewDrive · github.com/BoujeeEnjinia1701/dewdrive

REV	DESCRIPTION	DATE	BY
P1	Making sketch for the prototype build plan	2026-10-01	AC

TOP VIEW

Scale 1:10; looking down (along -Z)

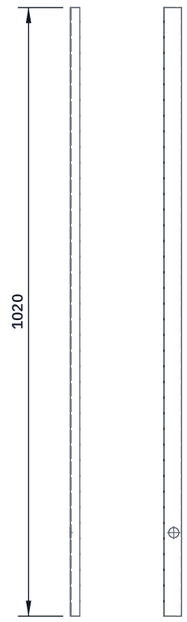

FRONT VIEW

Scale 1:10; looking at the front (along +Y)

RIGHT VIEW

Scale 1:10; looking at the right side (along -X)

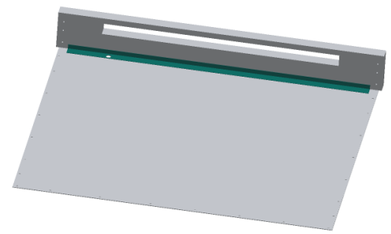

WHERE IT GOES

This part in colour, its neighbours in grey

HOW TO MAKE IT AND HOW IT FITS

Blank 1,020 x 47 x 1 mm. Fold 16 mm up along one long edge: a 30 mm flange and a 16 mm upstand.

Drill 17 mm through the flange for the drain fitting, 370 east of the centre (880 from the west end), 17 from the back of the upstand.

Fit: inside the box along the south (low) wall, the flange flat on the plate and the upstand against the wall, bedded in food-grade silicone; seal both ends to the east and west walls.

Water runs down the plate, over the flange edge into the corner and out through the fitting.

Check: no light under the flange when bedded.

DEWDRIVE

github.com/BoujeeEnjinia1701/dewdrive

DewDrive gutter: making sketch

DRAWING NO.	REV	SHEET	SIZE
DWD-DWG-105	P1	1 of 1	ANSI B

SCALE	UNITS	PROJECTION	DATE	DRAWN
1:10	mm		2026-10-01	Amish Chadha

MATERIAL / NOTES

Aluminium sheet 1 mm

Licensed CERN-OHL-S-2.0 · Design Molecule Lab · designmolecule.com

Generated from cad/src; do not edit by hand