BUILD PLAN SKETCH, PLAN NOT YET BUILT

DewDrive · github.com/BoujeeEnjinia1701/dewdrive

REV	DESCRIPTION	DATE	BY
P1	Making sketch for the prototype build plan	2026-10-01	AC

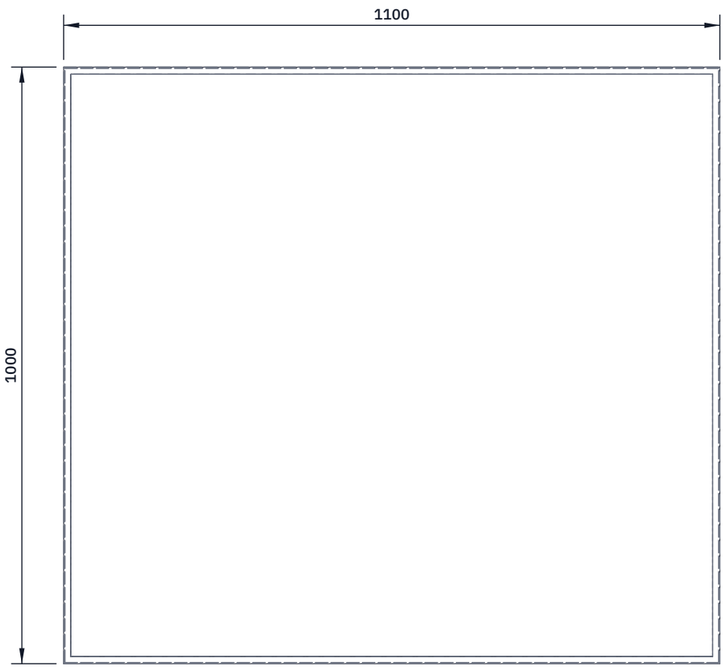

TOP VIEW

Scale 1:10; looking down (along -Z)

FRONT VIEW

Scale 1:10; looking at the front (along +Y)

RIGHT VIEW

Scale 1:10; looking at the right side (along -X)

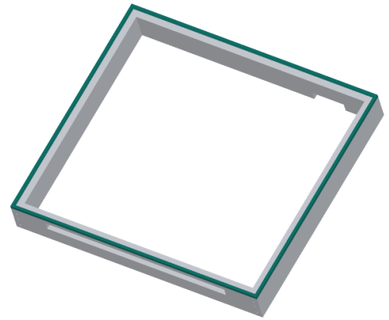

WHERE IT GOES

This part in colour, its neighbours in grey

HOW TO MAKE IT AND HOW IT FITS

Four lengths of U-channel, mitred 45 degrees: two 1,100 (north and south), two 1,000 (east and west), outside sizes.

Slide them onto the polycarbonate sheet (1,096 x 996, flutes running north to south); seal the low (south) flute ends with breather tape and the high ends with aluminium tape first.

Join each corner with a 20 x 20 x 2 angle bracket inside the channel web, two 3.2 mm rivets each side.

Hinges: three 60 mm stainless butt hinges on the north side, 440 west of centre, at centre and 470 east; rivet one leaf to the frame and screw the other into the north wall's top batten.

Latches: two over-centre latches on the south side, 475 each side of centre; keeper riveted to the frame, body screwed to the wall.

Fit: the frame rests on an EPDM seal on the wall tops.

Check: the lid closes evenly on the seal all round.

DEWDRIVE

github.com/BoujeeEnjinia1701/dewdrive

DewDrive lid frame: making sketch

DRAWING NO.	REV	SHEET	SIZE
DWD-DWG-111	P1	1 of 1	ANSI B

SCALE	UNITS	PROJECTION	DATE	DRAWN
1:10	mm		2026-10-01	Amish Chadha

MATERIAL / NOTES

Aluminium glazing U-channel 14 x 12 x 2 mm (for 10 mm sheet)

Licensed CERN-OHL-S-2.0 · Design Molecule Lab · designmolecule.com

Generated from cad/src; do not edit by hand