

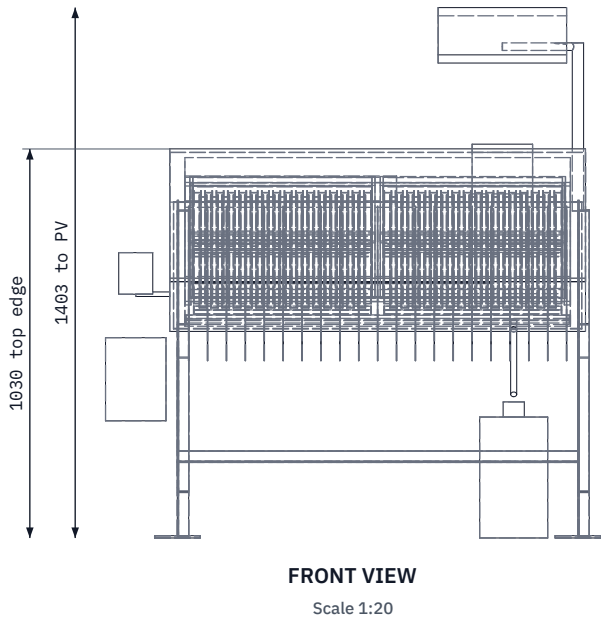



CONCEPT, NOT FOR FABRICATION

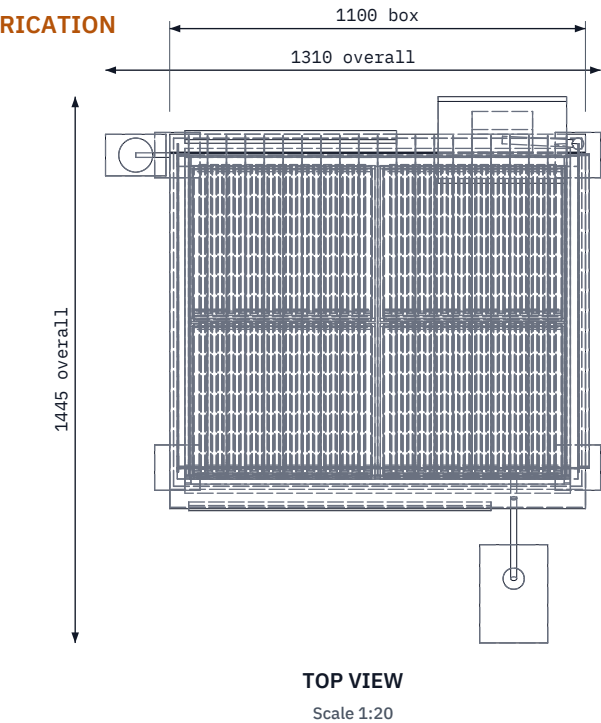

Glazing tilted 20 deg, facing the equator

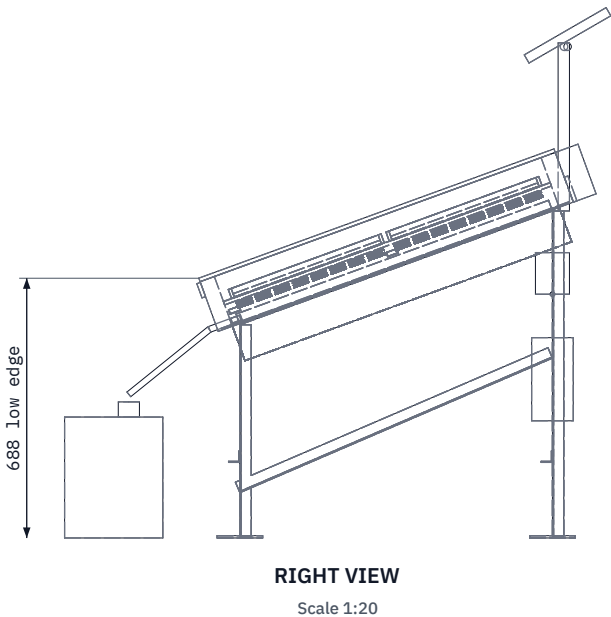

REV	DESCRIPTION	DATE	BY
P1	Preliminary GA for TRL 3 (from cad/src/model.py)	2026-09-25	AC
P2	Through-flow trays, baffle, raised inlet, drip screens (DDR-002)	2026-09-25	AC

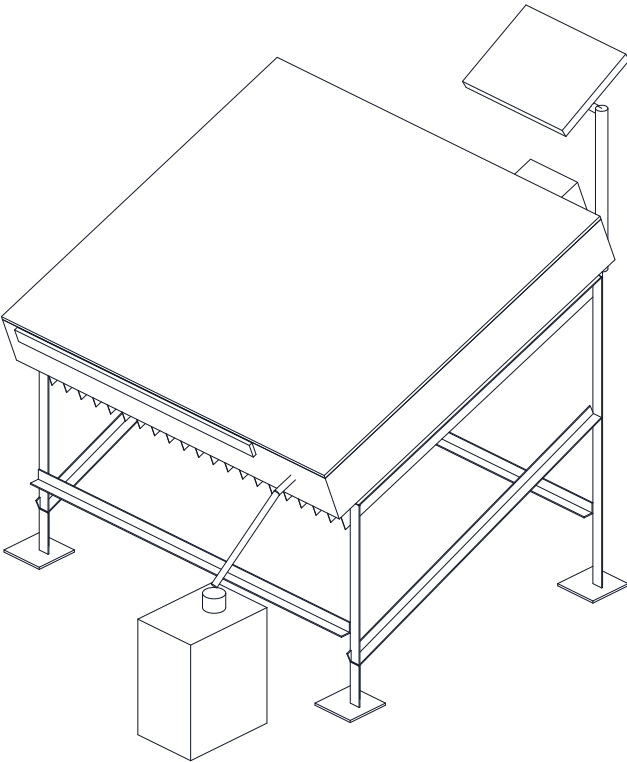

ISOMETRIC VIEW
Not to scale

MAIN DIMENSIONS AND INTERFACES (MM)

Box 1100 x 1000 x 140; walls 40 (ply, 25 PIR, ply)
Lid 10 twin-wall PC, hinged north edge; inner 1020 x 920
Trays 4 x 490 x 430 x 25, sealed on a baffle; bed 9.3 deep, 0.785 m²
Drip screens: 2 layers of 20 x 6 channels at 30 pitch; sumps 0.58 L
Gaps: 45 tray rim to lid, 65 tray floor to condenser
Condenser 2 Al plate, 21 fins 1 x 100 at 50 pitch
Inlet 800 x 40 (S, above trays); outlet 560 x 70 and fan (N, below)
Stand 4 legs, L30 x 3 galv.; feet 120 sq; 2 ground anchors
Mass about 54 kg dry; box about 33 kg (DWD-CAL-001 v0.2, G1)
Third-angle; front view from south (-Y), right from +X

DEWDRIVE

General arrangement

DRAWING NO. DWD-DWG-001			REV P2	SHEET 1 of 1	SIZE ANSI B
SCALE 1:20	UNITS mm	PROJECTION 	DATE 2026-09-25		DRAWN Amish Chadha
MATERIAL / NOTES Plywood and PIR box, twin-wall PC lid, Al trays and finned condenser, galv. steel stand; see bom/bom.csv. PRELIMINARY, NOT FOR FABRICATION					
Licensed CERN-OHL-S-2.0 · Design Molecule Lab · designmolecule.com				Generated from cad/src; do not edit by hand	